
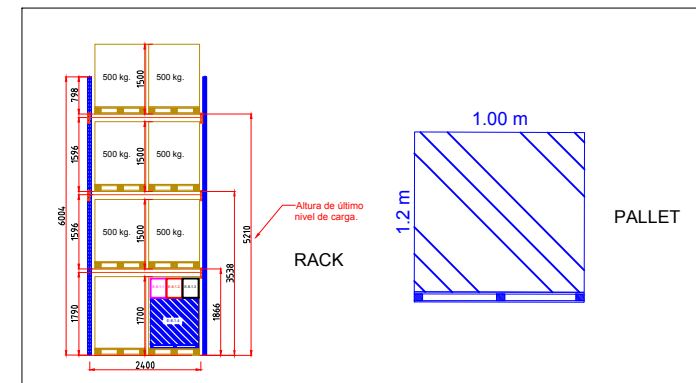


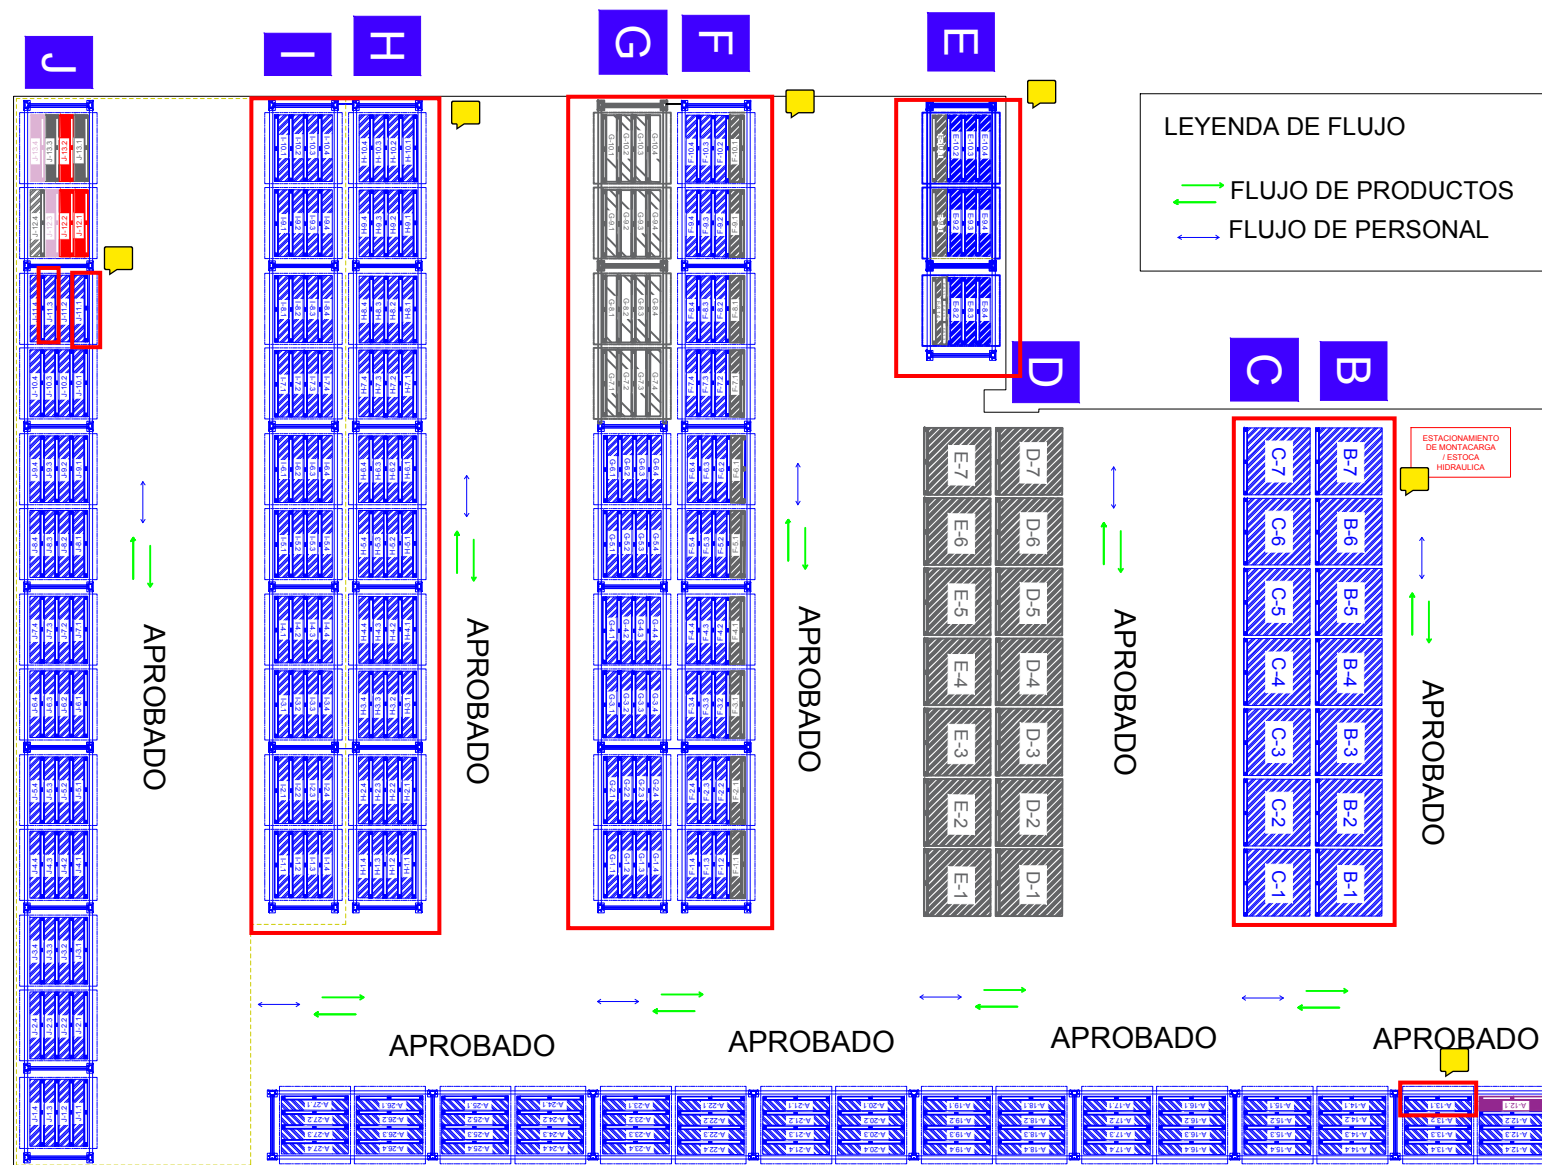

Área exclusiva para DIPHASAC SAC				
NOMBRE DEL ÁREA	DIMENSIONES	POSICIÓN	CANTIDAD	VOLUMEN
APROBADOS	1.2m x 1m x 1.5m	A-13.1 al A-27.1, A-10.2 al A-27.2, A-10.3 al A-27.3, A-10.4 al A-27.4, H-1.1 al H-10.1, H-1.2 al H-10.2, H-1.3 al H-10.3, H-1.4 al H-10.4, E-8.2 al E-10.2, E-8.3 al E-10.3, E-8.4 al E-10.4, F-1.2 al F-10.2, F-1.3 al F-10.3, F-1.4 al F-10.4, G-1.1 al G-6.1, G-1.2 al G-6.2, G-1.3 al G-6.3, G-1.4 al G-6.4.	172 pallets rack	309.60 m3
	1.2m x 1m x 1.7m		14 pallets	28.56 m3
APROBADOS/CONTROLADOS	1.2m x 1m x 1.5m	J-1.1 al J-11.1, J-1.2 al J-11.2, J-1.3 al J-11.3, J-1.4 al J-11.4, I-1.1 al I-10.1, I-1.2 al I-10.2, I-1.3 al I-10.3, I-1.4 al I-10.4	84 pallets rack	151.2 m3
TOTAL DE APROBADOS/APROBADOS CONTROLADOS: 489.36m3				
CONTRAMUESTRA	1.2m x 1m x 1.5m	J-12.3, J-13.4	2 pallets rack	3.60 m3
BAJAS/ RECHAZADOS	1.2m x 1m x 1.5m	J-12.1, J-12.2, J-13.2	3 pallets rack	5.40 m3
DEVOLUCIONES	1.2m x 1m x 1.5m	A-10.1, A-12.1	2 pallets rack	3.60 m3
TOTAL DE ÁREAS EXCLUSIVAS: 501.96 m3				
Área compartida para todos los usuarios del almacén				
NOMBRE DEL ÁREA	Dimensiones	Posición	Cantidad	Volumen
RECEPCIÓN	1.20m x 1m x 1.70m	A-1 al A-5	5 pallets	11.32 m3
	1.09m x 1.15m x 0.89m	A-M1	1 mesa	
CUARENTENA	1.20m x 1m x 1.70m	A-6 al A-9	4 pallets	8.16 m3
EMBALAJE	0.65m x 0.90m x 2m	K-M2	1 mesa	1.17 m3
DESPACHO	1.20m x 1m x 1.70m	K-1 al K-7	7 pallets	14.28 m3
ADMINISTRATIVA	5.80m x 2m x 4m	-----	1 unidad	46.40 m3

PLANOS: DISTRIBUCIÓN INTERNA ALMACÉN	
USUARIO:	DIPHASAC S.A.C.
PROPIETARIO: LOGISSA S.A.C.	
UBICACIÓN: CAR.PANAMERICANA SUR, KM 29.5 INT. A-8 LIMA - LIMA - LURIN	

RESPONSABLES	FECHA	V"B"
ELABORADO POR: ARANDA MOSTACERO, MARGARETH	4/30/2026	
REVISADO POR Q.F.: REMÓN CHOCCE, ELIZABETH	4/30/2026	
APROBADO POR: GONZALES MORALES, SEBASTIAN	4/30/2026	

Revisado por: Q.F. ZAPATA REYES, KATIA